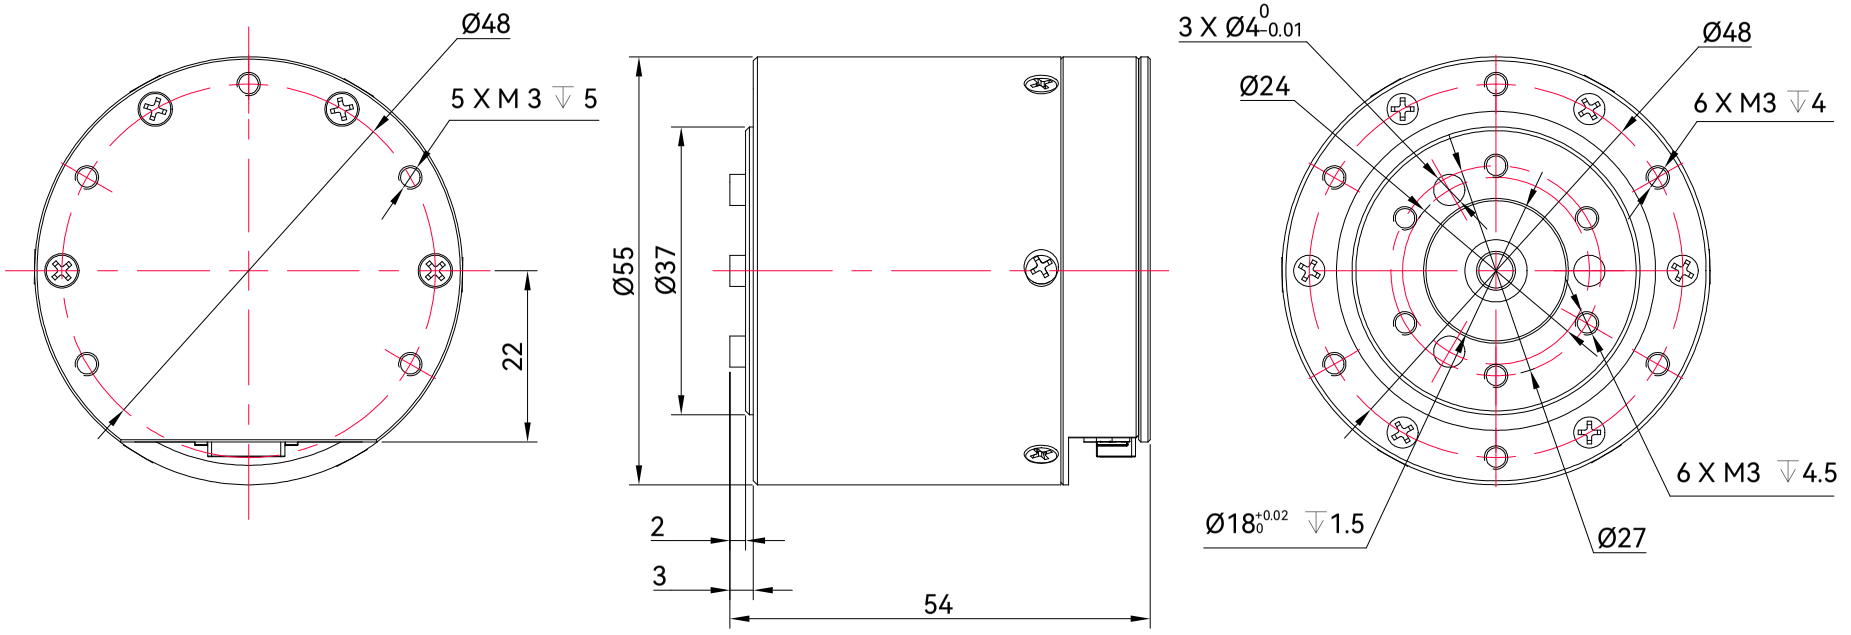

Ø48
5 X M 3 ↧ 5
22
Ø55
Ø37
2
3
54
3 X Ø4 0 -0.01
Ø24
Ø48
6 X M3 ↧4
6 X M3 ↧4.5
Ø18 +0.02 0 ↧1.5
Ø27